



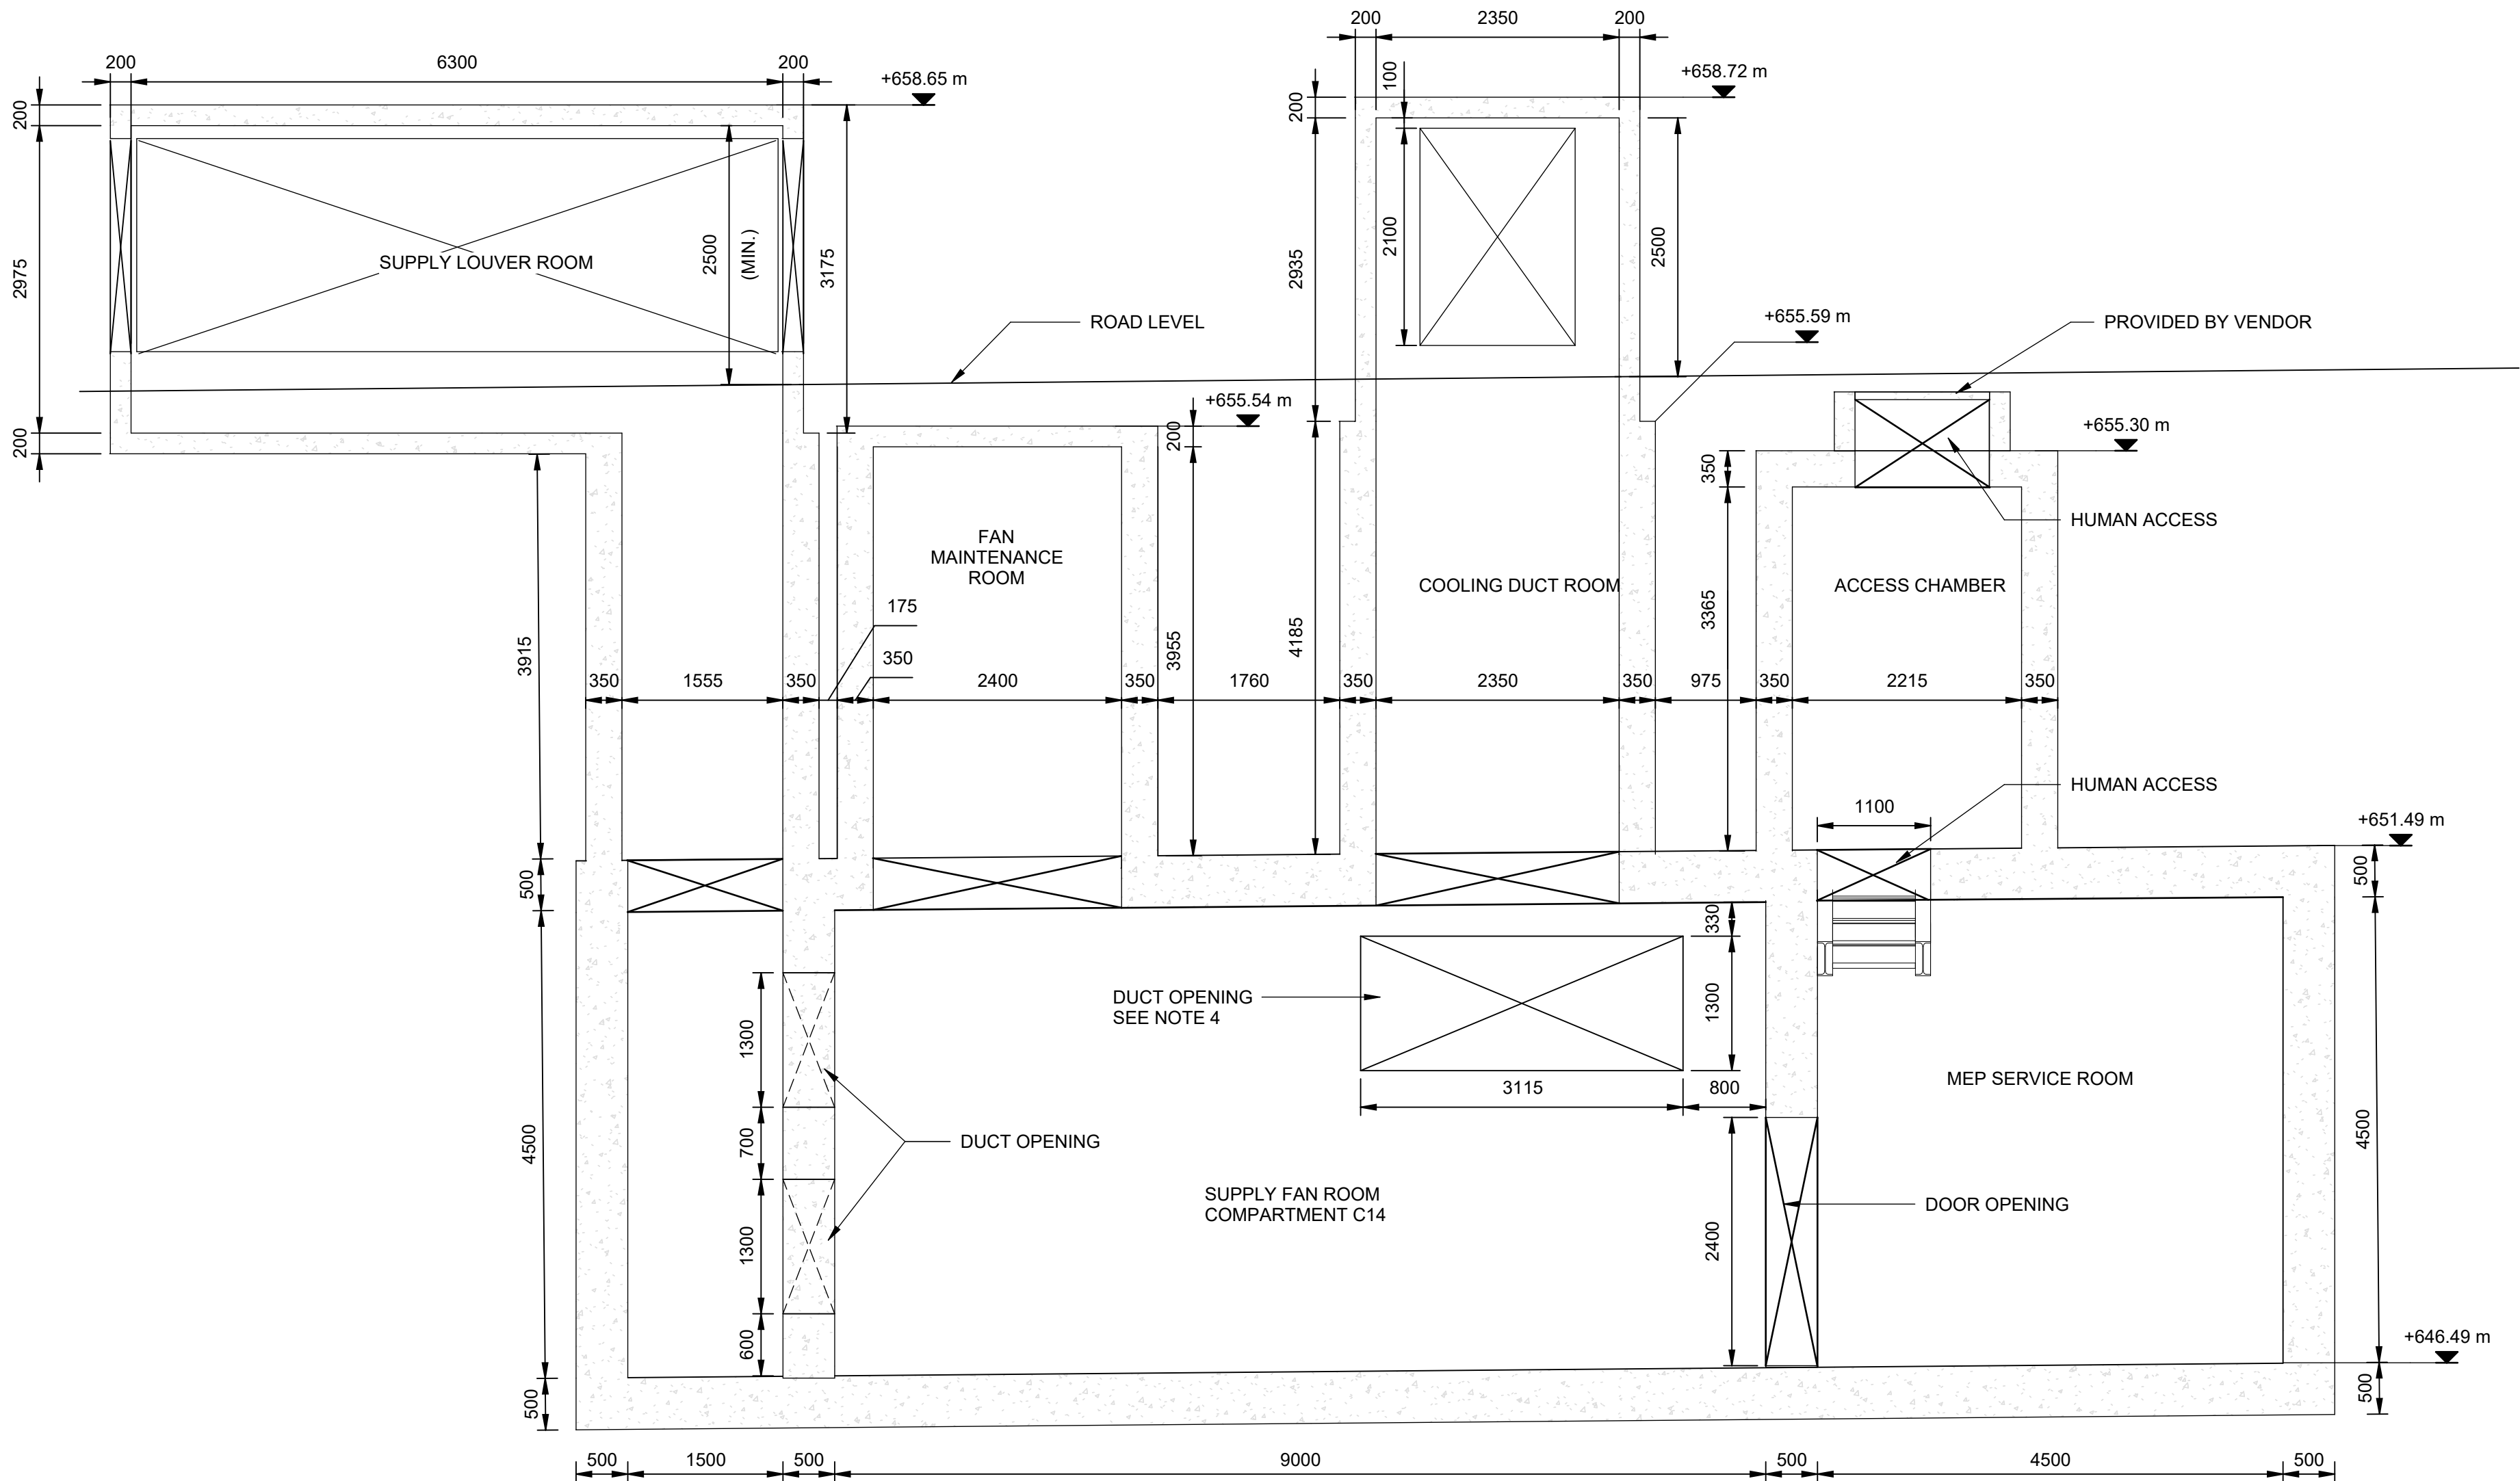

3 SECTION
1 : 50

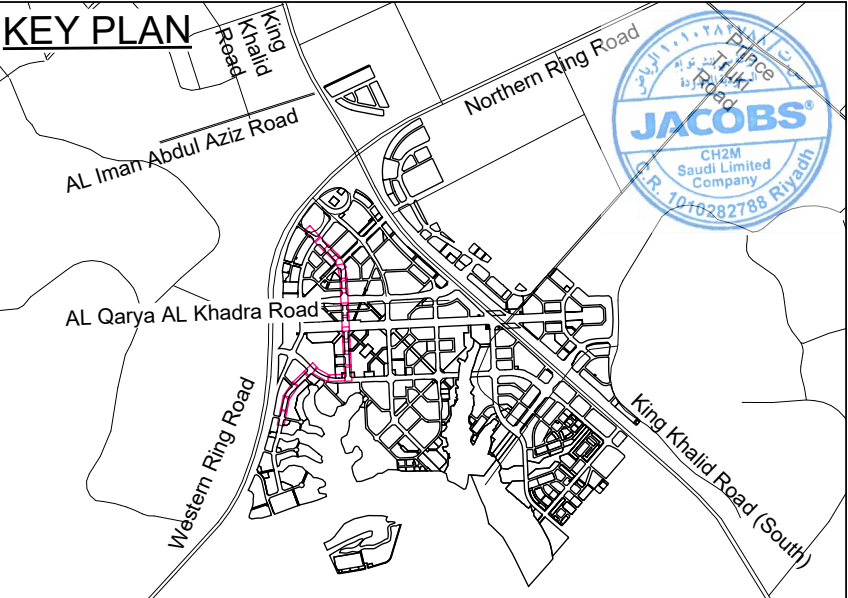

ORIENTATION		DATUM
		GEODETIC DATUM: WGS-84 PROJECT SYSTEM: UTM ZONE: 38N

- GENERAL NOTES**
- ALL LEVELS ARE IN METERS AND ALL DIMENSIONS ARE IN MILLIMETERS UNLESS OTHERWISE NOTED.
 - ALL DIMENSIONS SHALL BE CHECKED AND VERIFIED ON SITE BY THE SUB-CONTRACTOR/CONSTRUCTION CONTRACTOR AND ANY DISCREPANCIES SHALL BE REPORTED TO SITE-IN- CHARGE.
 - SAFE BEARING CAPACITY CONSIDERED IN DESIGN AS 700kN/m² AS PER GEOTECHNICAL DOCUMENT NO: IP-INF-053-0000-JCB-RPT-GE-000001.
 - CONTRACTORS TO CONFIRM THE LOCATION AND SIZE OF OPENINGS FROM ENGINEER ON SITE PRIOR TO PROCUREMENT AND INSTALLATION OF VENDOR EQUIPMENT. CONTRACTOR TO CONFIRM THE LOCATION
 - FOR SUMP PIT DETAILS REFER TO DRAWING IP-INF-054-0000-JCB-DWG-ST-400-2000401.
 - FOR OPENINGS EQUAL TO OR SMALLER THAN 200 MM REFER RELEVANT HVAC / IC / DRAINAGE / ELECTRICAL INFRA / ELECTRICALMEP / FLS DRAWING.

- ABBREVIATION:**
- PSS - PRIMARY SUBSTATION
 - SSL - STRUCTURAL SLAB LEVEL
 - IL - INVERT LEVEL
 - CJ - CONSTRUCTION JOINT
 - TOW - TOP OF WALL
 - BOW - BOTTOM OF WALL
 - TOB - TOP OF BEAM
 - NF - NEAR FACE (IN CONTACT WITH SOIL)
 - FF - FAR FACE (IN CONTACT WITH WATER)
 - EF - EACH FACE
 - GL - GROUND LEVEL
 - THK - THICKNESS
 - CB - CONCEAL BEAM

PROJECT STAGE: ISSUED FOR CONSTRUCTION

THE USE OF THIS DOCUMENT FOR CONSTRUCTION PURPOSES IS SUBJECT TO AND CONDITIONAL UPON RECEIPT OF THE APPROPRIATE STATUTORY AUTHORITY APPROVAL

ISSUED FOR CONSTRUCTION	01	10/04/2025	AAJ
ISSUED FOR CONSTRUCTION (CONDITIONAL)	00	10/02/2025	AAJ
DESCRIPTION	REV	DATE	AUTHORISED

PROJECT:

**DIRIYAH GATE PHASE II
& KING KHALID ROAD
INFRASTRUCTURE DESIGN
KINGDOM OF SAUDI ARABIA**

CLIENT:

DIRIYAH COMPANY
8500 Prince Sattam Ibn Abdulaziz
Al Shohda Dist. AD DIRIYAH 12572 - 4000
Kingdom Of Saudi Arabia

LEAD CONSULTANT:

Jacobs
P.O. Box 360, Dubai U.A.E.
www.jacobs.com

Jacobs

SUBCONSULTANT:

PACKAGE:

**DG II - INFRA PACKAGE - 1
DD-2023-118**

DRAWING TITLE:

**L-SECTION
FAN ROOM AT C14 (TYPE 2)**

DRAWN	CHECKED	VERIFIED	APPROVED	SIZE
GB	AD/SS	AS/VB	AAJ	A1
DATE:	DATE:	DATE:	DATE:	SCALE
10/04/2025	10/04/2025	10/04/2025	10/04/2025	1:50

DRAWING NUMBER:

IP-INF-054-0000-JCB-DWG-ST-400-2000425

Rev

01