



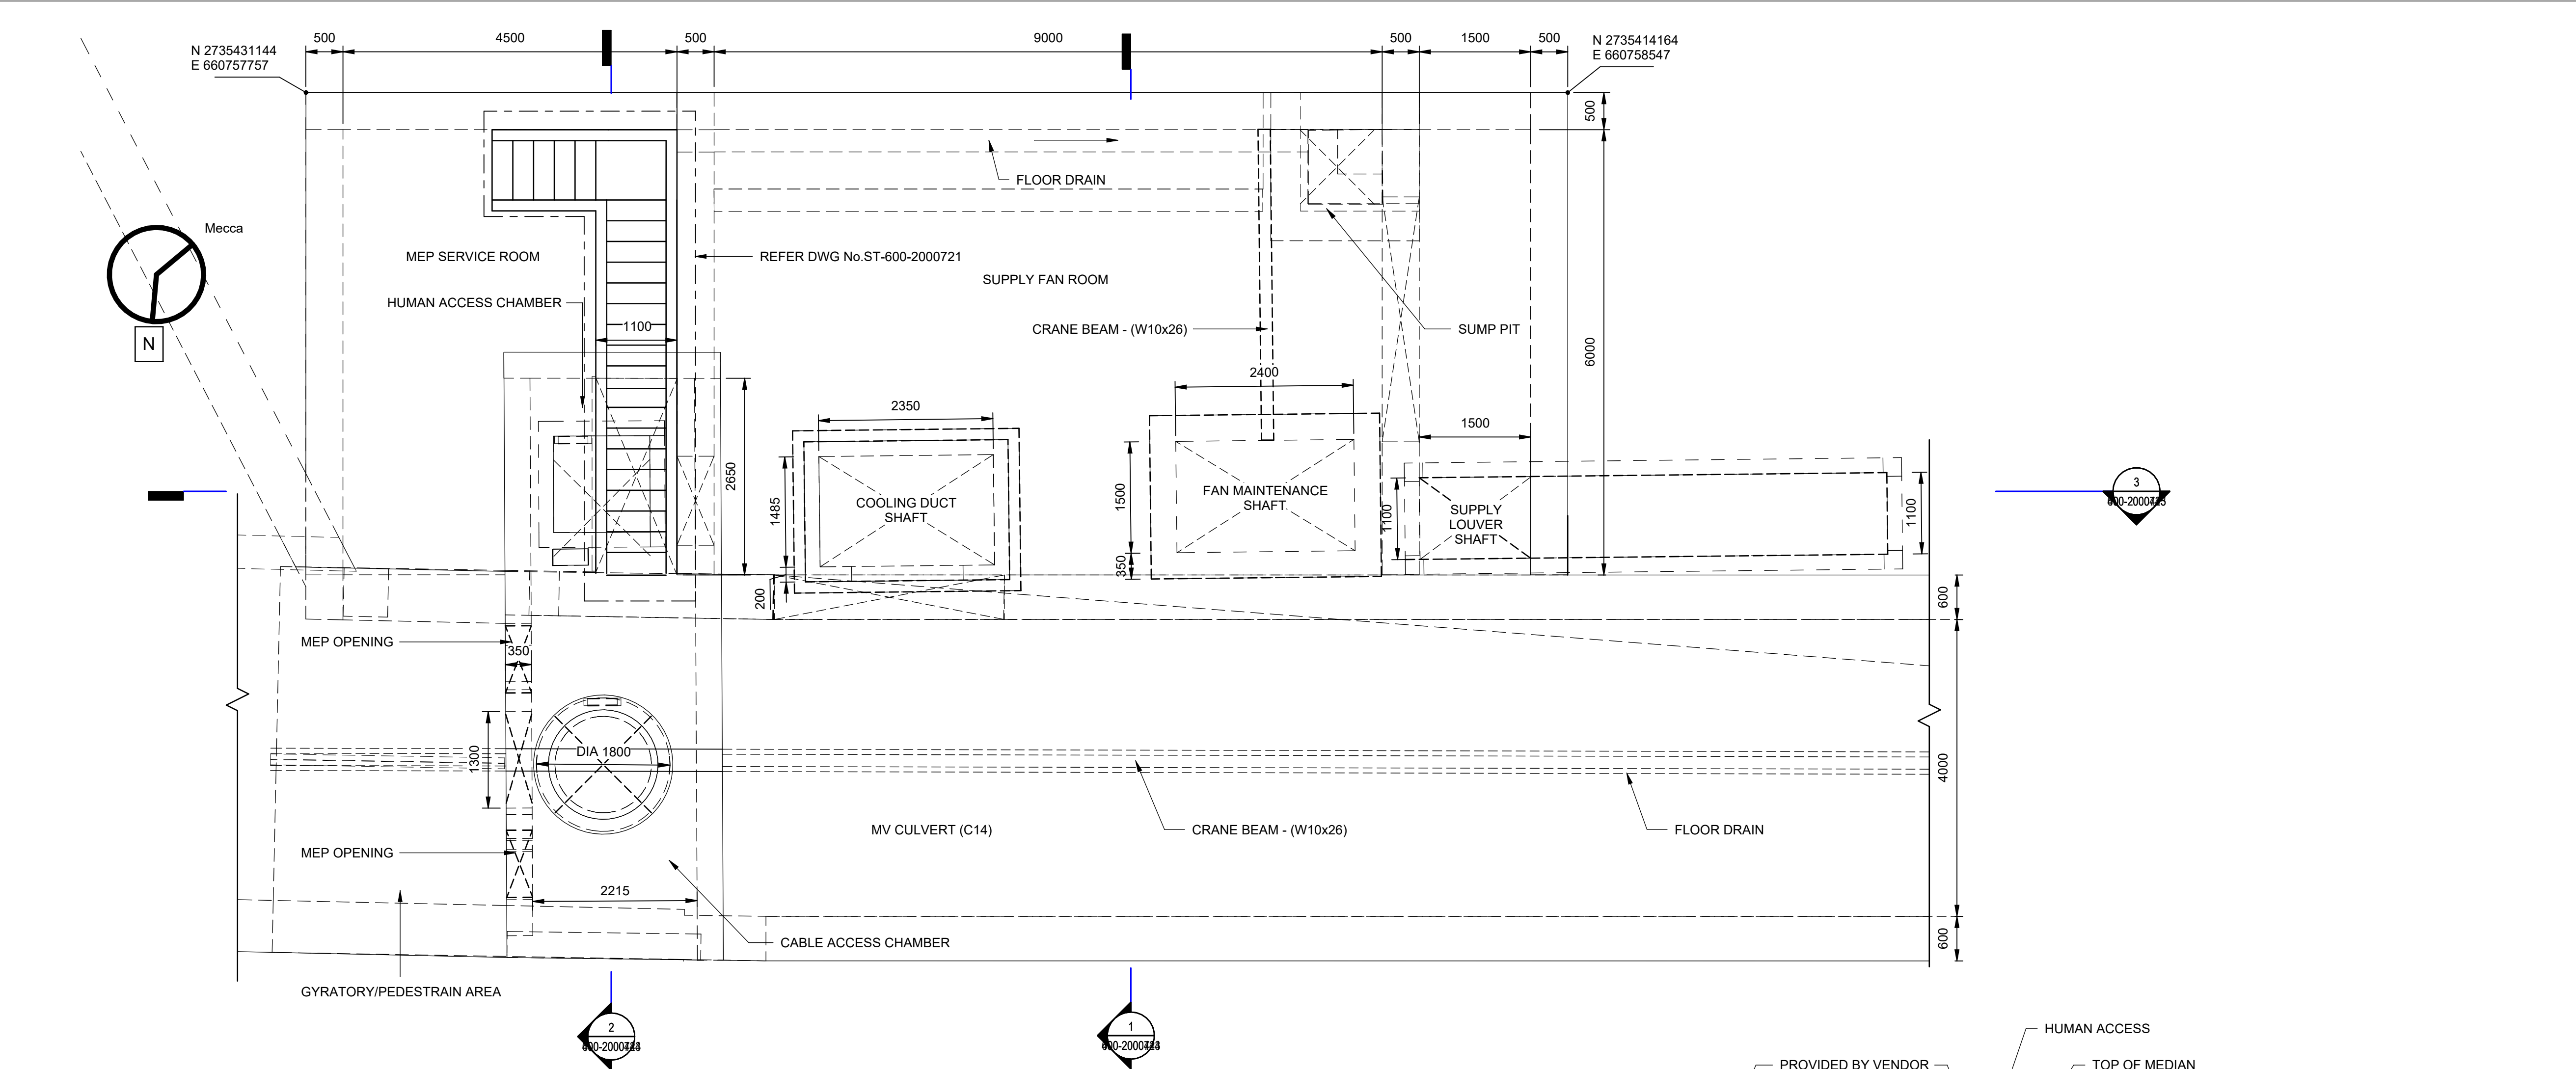


ENLARGED PLAN - FAN ROOM AT C14 (TYPE 2)

1 : 50


FOR LOCATION OF THE FAN ROOM REFER TO IP-INF-054-0000-JCB-DWG-ST-200-2000113

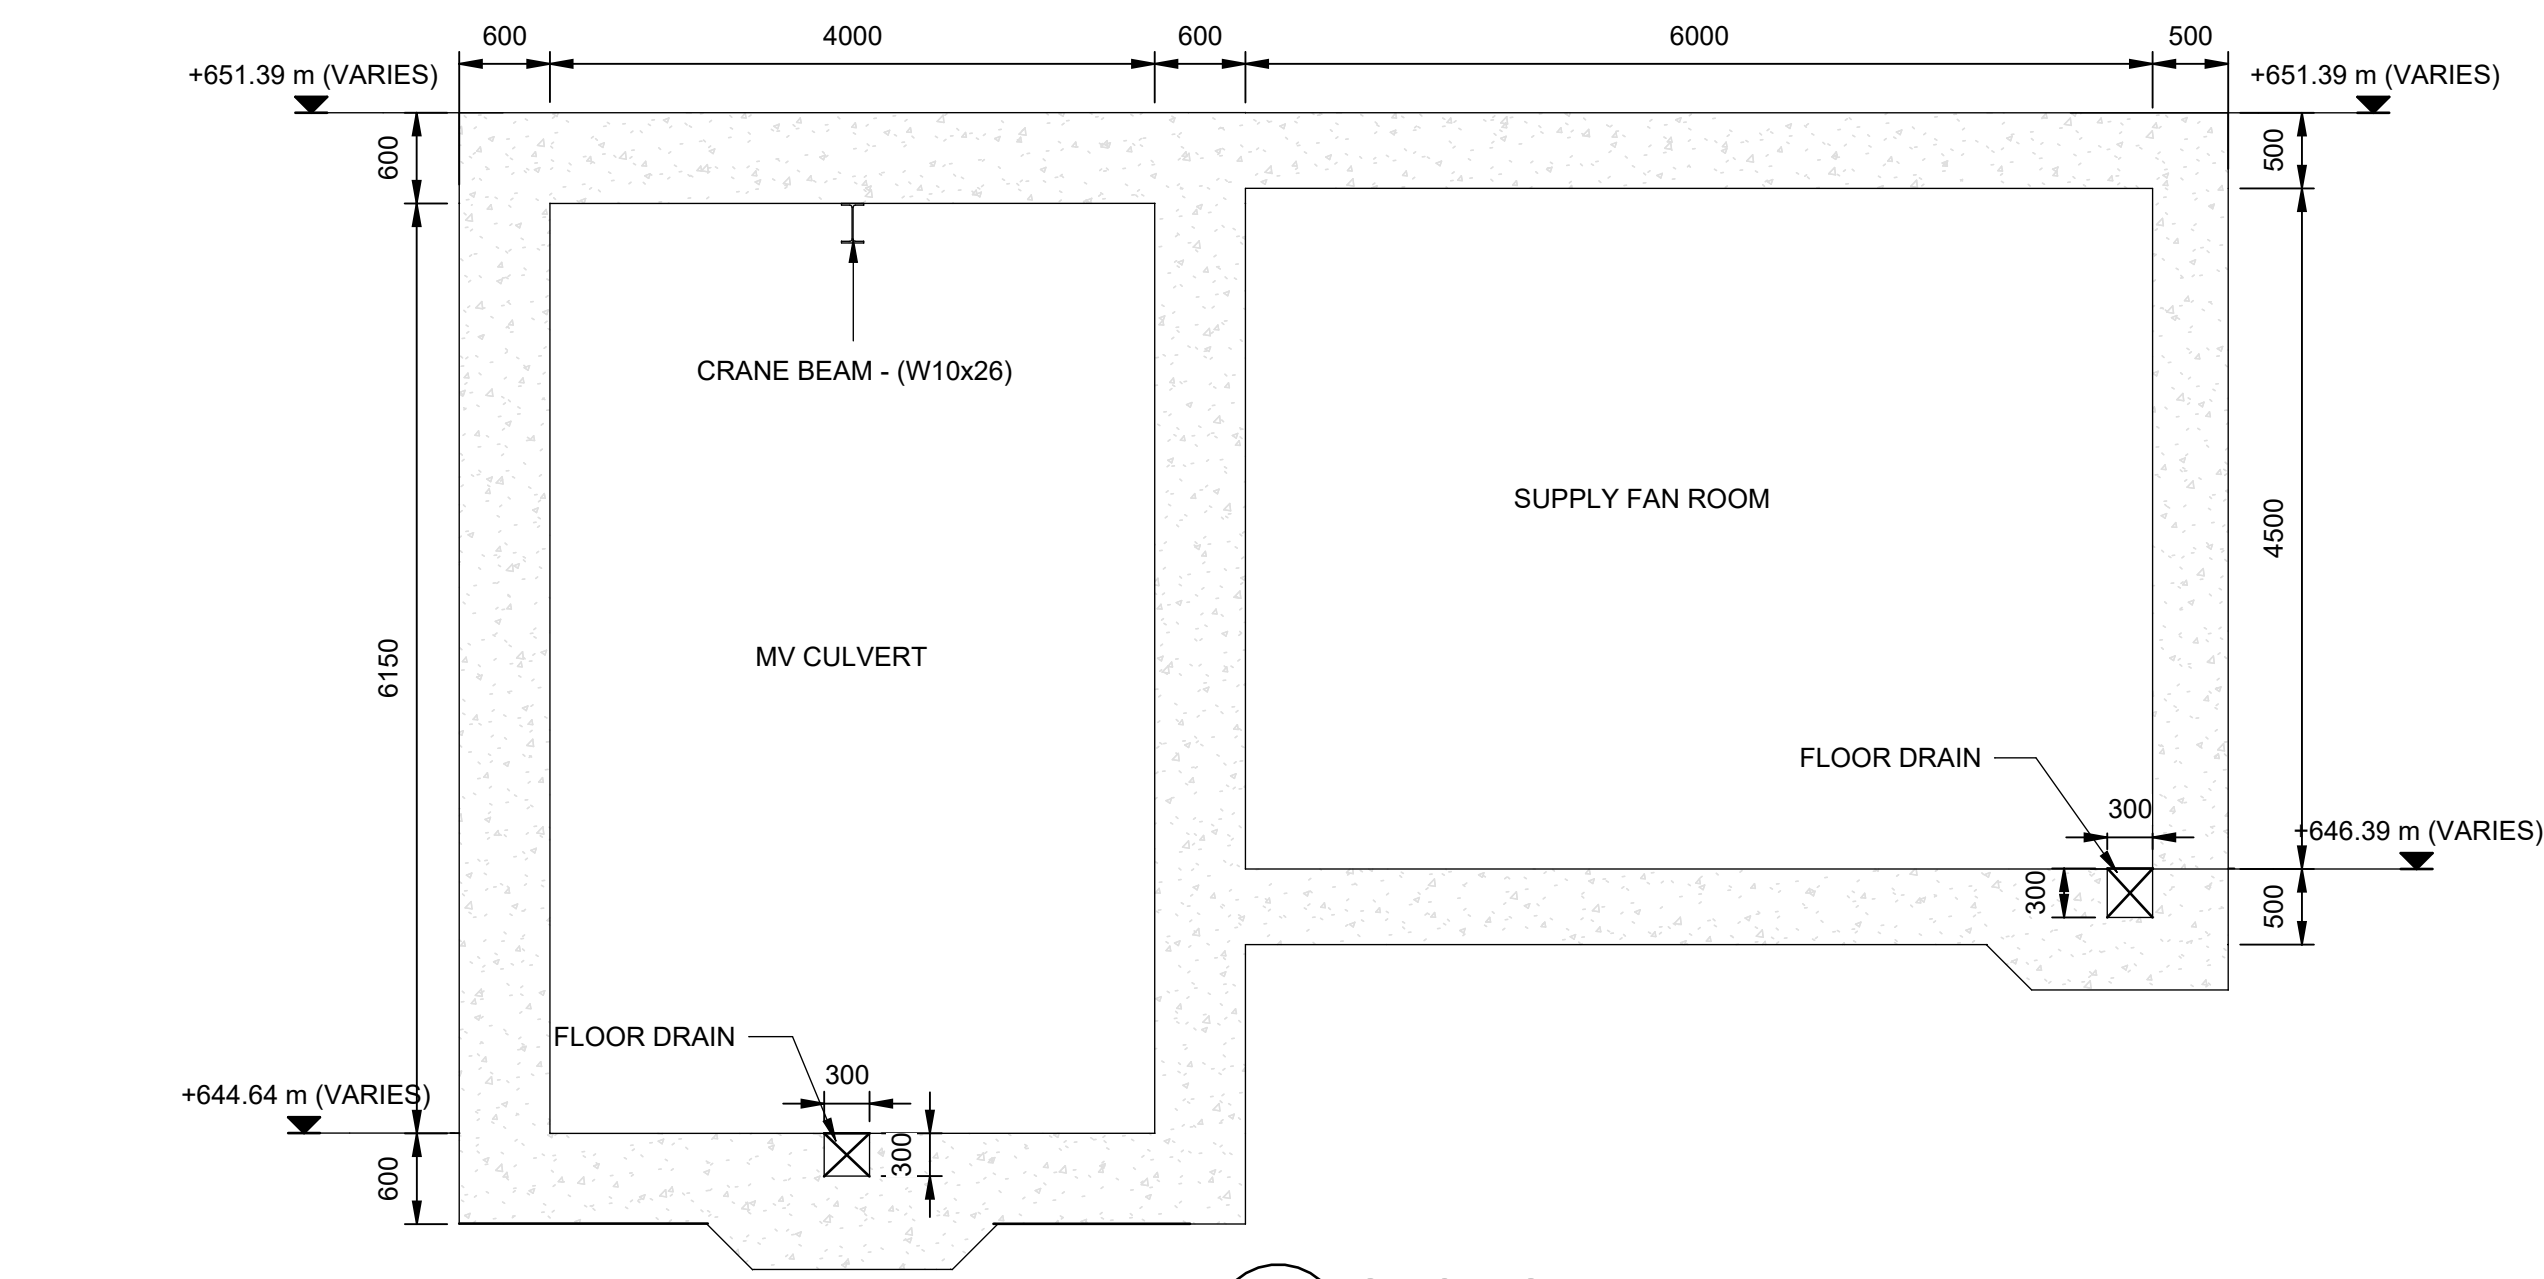

1 SECTION
1 : 50

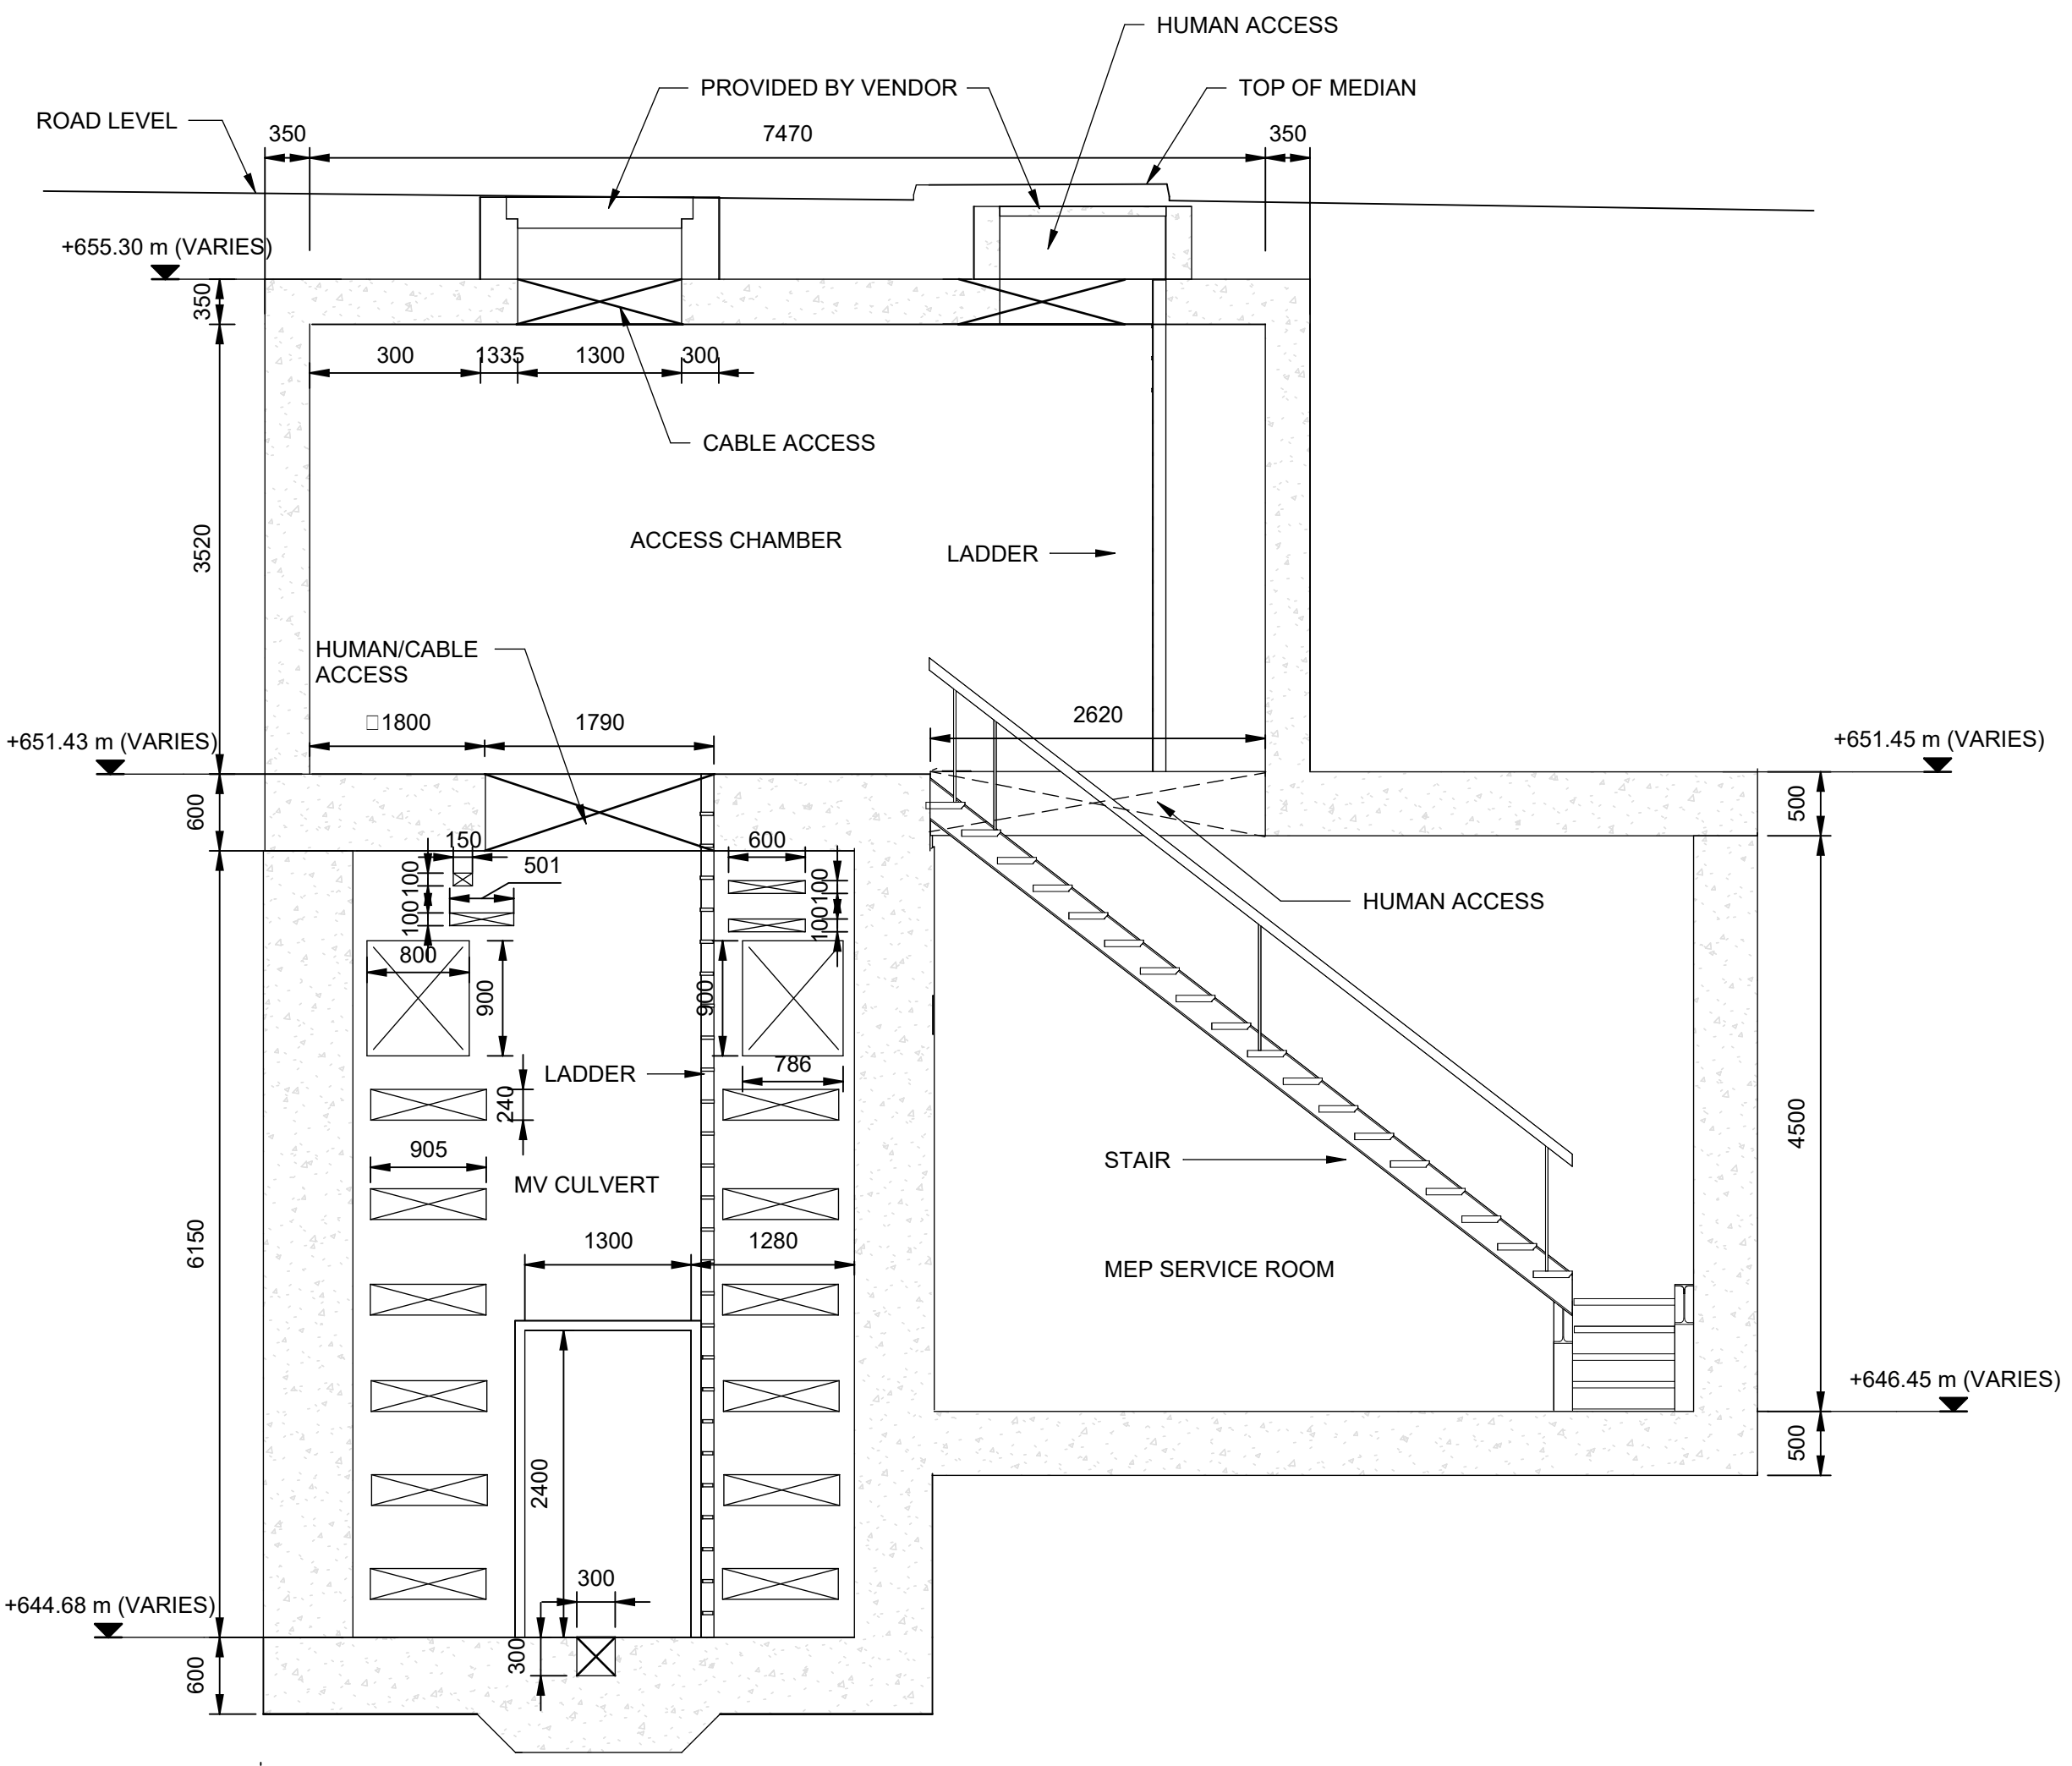

2 SECTION
1 : 50

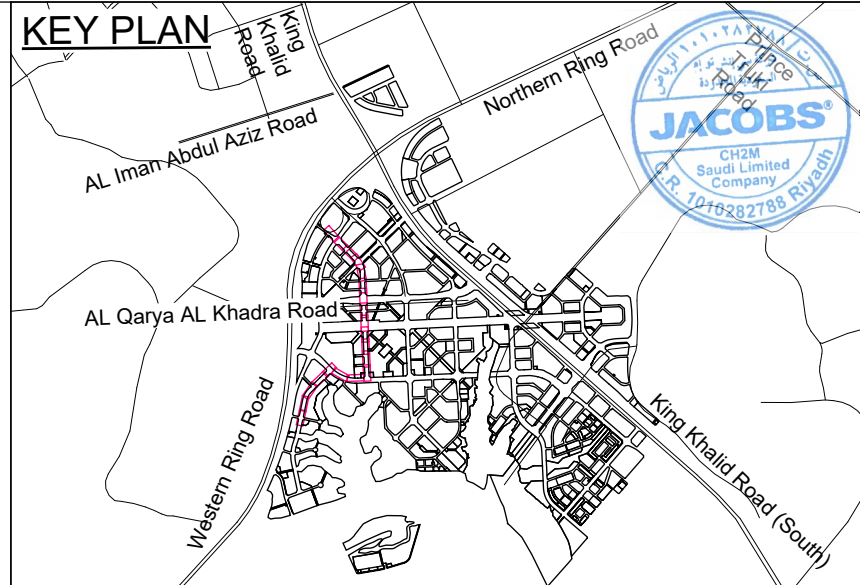

ORIENTATION	DATUM
Mecca	GEODETIC DATUM: WGS-84 PROJECT SYSTEM: UTM ZONE: 38N

- GENERAL NOTES**
- ALL LEVELS ARE IN METERS AND ALL DIMENSIONS ARE IN MILLIMETERS UNLESS OTHERWISE NOTED.
 - ALL DIMENSIONS SHALL BE CHECKED AND VERIFIED ON SITE BY THE SUB-CONTRACTOR/CONSTRUCTION CONTRACTOR AND ANY DISCREPANCIES SHALL BE REPORTED TO SITE-IN-CHARGE.
 - SAFE BEARING CAPACITY CONSIDERED IN DESIGN AS 700KN/m² AS PER GEOTECHNICAL DOCUMENT NO: IP-INF-053-0000-JCB-RPT-GE-000001.
 - CONTRACTORS TO CONFIRM THE LOCATION AND SIZE OF OPENINGS FROM ENGINEER ON SITE PRIOR TO PROCUREMENT AND INSTALLATION OF VENDOR EQUIPMENT. CONTRACTOR TO CONFIRM THE LOCATION FOR SUMP PIT DETAILS REFER TO DRAWING IP-INF-054-0000-JCB-DWG-ST-400-2000401.
 - FOUNDATION AT DIFFERENT LEVELS SHOULD BE SET ON ROCK, AND ANY OVER EXCAVATION SHOULD BE FILLED WITH MASS/CYCLOPEAN CONCRETE.
 - FOR OPENINGS EQUAL TO OR SMALLER THAN 200 MM REFER RELEVANT HVAC / IC / DRAINAGE / ELECTRICAL INFRA / ELECTRICALMEP / FLS DRAWING.

ABBREVIATION:

PSS - PRIMARY SUBSTATION
SSL - STRUCTURAL SLAB LEVEL
IL - INVERT LEVEL
CJ - CONSTRUCTION JOINT
TOW - TOP OF WALL
BOW - BOTTOM OF WALL
TOB - TOP OF BEAM
NF - NEAR FACE (IN CONTACT WITH SOIL)
FF - FAR FACE (IN CONTACT WITH WATER)
EF - EACH FACE
GL - GROUND LEVEL
THK - THICKNESS
CB - CONCEAL BEAM

PROJECT STAGE: ISSUED FOR CONSTRUCTION

THE USE OF THIS DOCUMENT FOR CONSTRUCTION PURPOSES IS SUBJECT TO AND CONDITIONAL UPON RECEIPT OF THE APPROPRIATE STATUTORY AUTHORITY APPROVAL

DESCRIPTION	REV	DATE	AUTHORISED
ISSUED FOR CONSTRUCTION	01	10/04/2025	AAJ
ISSUED FOR CONSTRUCTION (CONDITIONAL)	00	10/02/2025	AAJ

PROJECT:

**DIRIYAH GATE PHASE II
& KING KHALID ROAD
INFRASTRUCTURE DESIGN
KINGDOM OF SAUDI ARABIA**

CLIENT:

DIRIYAH COMPANY
8500 Prince Sattam Ibn Abdulaziz
Al Shohda Dist. AD DIRIYAH 12572 - 4000
Kingdom Of Saudi Arabia

LEAD CONSULTANT:

Jacobs
P.O. Box 360, Dubai U.A.E.
www.jacobs.com

SUBCONSULTANT:

PACKAGE:

**DG II - INFRA PACKAGE - 1
DD-2023-118**

DRAWING TITLE:

**ENLARGED PLAN AND SECTION
FAN ROOM AT C14 (TYPE 2)**

DRAWN	CHECKED	VERIFIED	APPROVED	SIZE
GB	AD/SS	AS/VB	AAJ	A1
DATE:	DATE:	DATE:	DATE:	SCALE
10/04/2025	10/04/2025	10/04/2025	10/04/2025	1:50

DRAWING NUMBER:

IP-INF-054-0000-JCB-DWG-ST-400-2000424

01