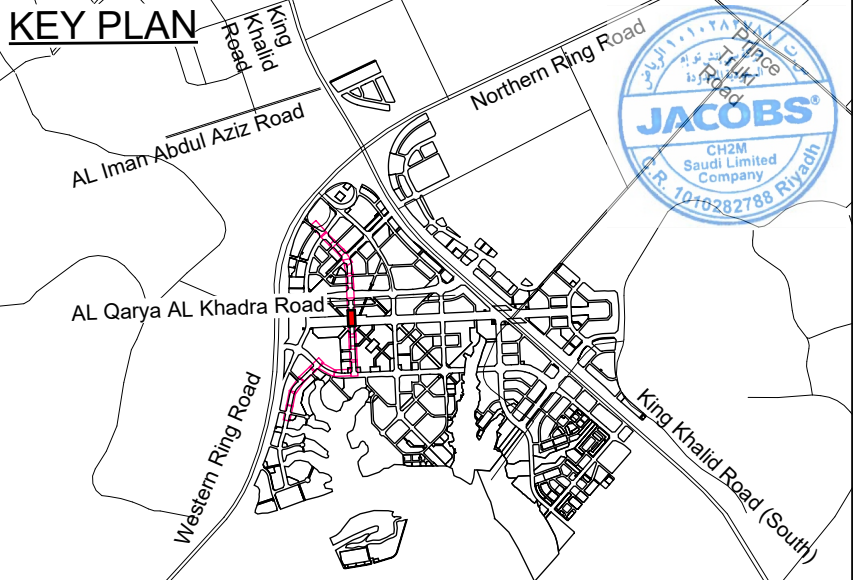


- GENERAL NOTES:
- ALL DIMENSIONS ARE IN MILLIMETER, ALL LEVELS ARE IN METERS UNLESS OTHERWISE INDICATED.
 - FOR EARTHING DETAILS SEE ELECTRICAL INFRA DRAWINGS
- IP-INF-054-0000-JCB-DWG-EL-200-3103001 TO
IP-INF-054-0000-JCB-DWG-EL-200-3103020
- ABBREVIATION:
- C - COMPARTMENT
TL - MV CULVERT LEVEL
RL - ROAD LEVEL
EJ - EXPANSION JOINT

- LEGEND
- EARTHING CONNECTION POINTS

PROJECT STAGE: ISSUED FOR CONSTRUCTION

THE USE OF THIS DOCUMENT FOR CONSTRUCTION PURPOSES IS SUBJECT TO AND CONDITIONAL UPON RECEIPT OF THE APPROPRIATE STATUTORY AUTHORITY APPROVAL

DESCRIPTION	REV	DATE	AUTHORISED
ISSUED FOR CONSTRUCTION	05	10/04/2025	AAJ
ISSUED FOR CONSTRUCTION (CONDITIONAL)	04	04/03/2025	AAJ
ISSUED FOR CONSTRUCTION (CONDITIONAL)	03	21/02/2025	AAJ
ISSUED FOR CONSTRUCTION (CONDITIONAL)	02	14/02/2025	AAJ
ISSUED FOR CONSTRUCTION (CONDITIONAL)	01	10/02/2025	AAJ
ISSUED FOR CONSTRUCTION (CONDITIONAL)	00	04/02/2025	AAJ

PROJECT:

**DIRIYAH GATE PHASE II
& KING KHALID ROAD
INFRASTRUCTURE DESIGN
KINGDOM OF SAUDI ARABIA**

CLIENT:

DIRIYAH COMPANY
8500 Prince Sattam Ibn Abdulaziz
Al Shohda Dist. AD DIRIYAH 12572 - 4000
Kingdom Of Saudi Arabia

LEAD CONSULTANT:

Jacobs
P.O. Box 360, Dubai U.A.E.
www.jacobs.com

Jacobs

SUBCONSULTANT:

PACKAGE:

**DG II - INFRA PACKAGE - 1
DD-2023-118**

DRAWING TITLE:

**MV CULVERT
STRUCTURAL LAYOUT PART -12**


DRAWN	CHECKED	VERIFIED	APPROVED	SIZE
AG	AD/SS	AS/VB	AAJ	A1
DATE:	DATE:	DATE:	DATE:	SCALE
10/04/2025	10/04/2025	10/04/2025	10/04/2025	1:200

DRAWING NUMBER:

IP-INF-054-0000-JCB-DWG-ST-200-2000112


Rev

05

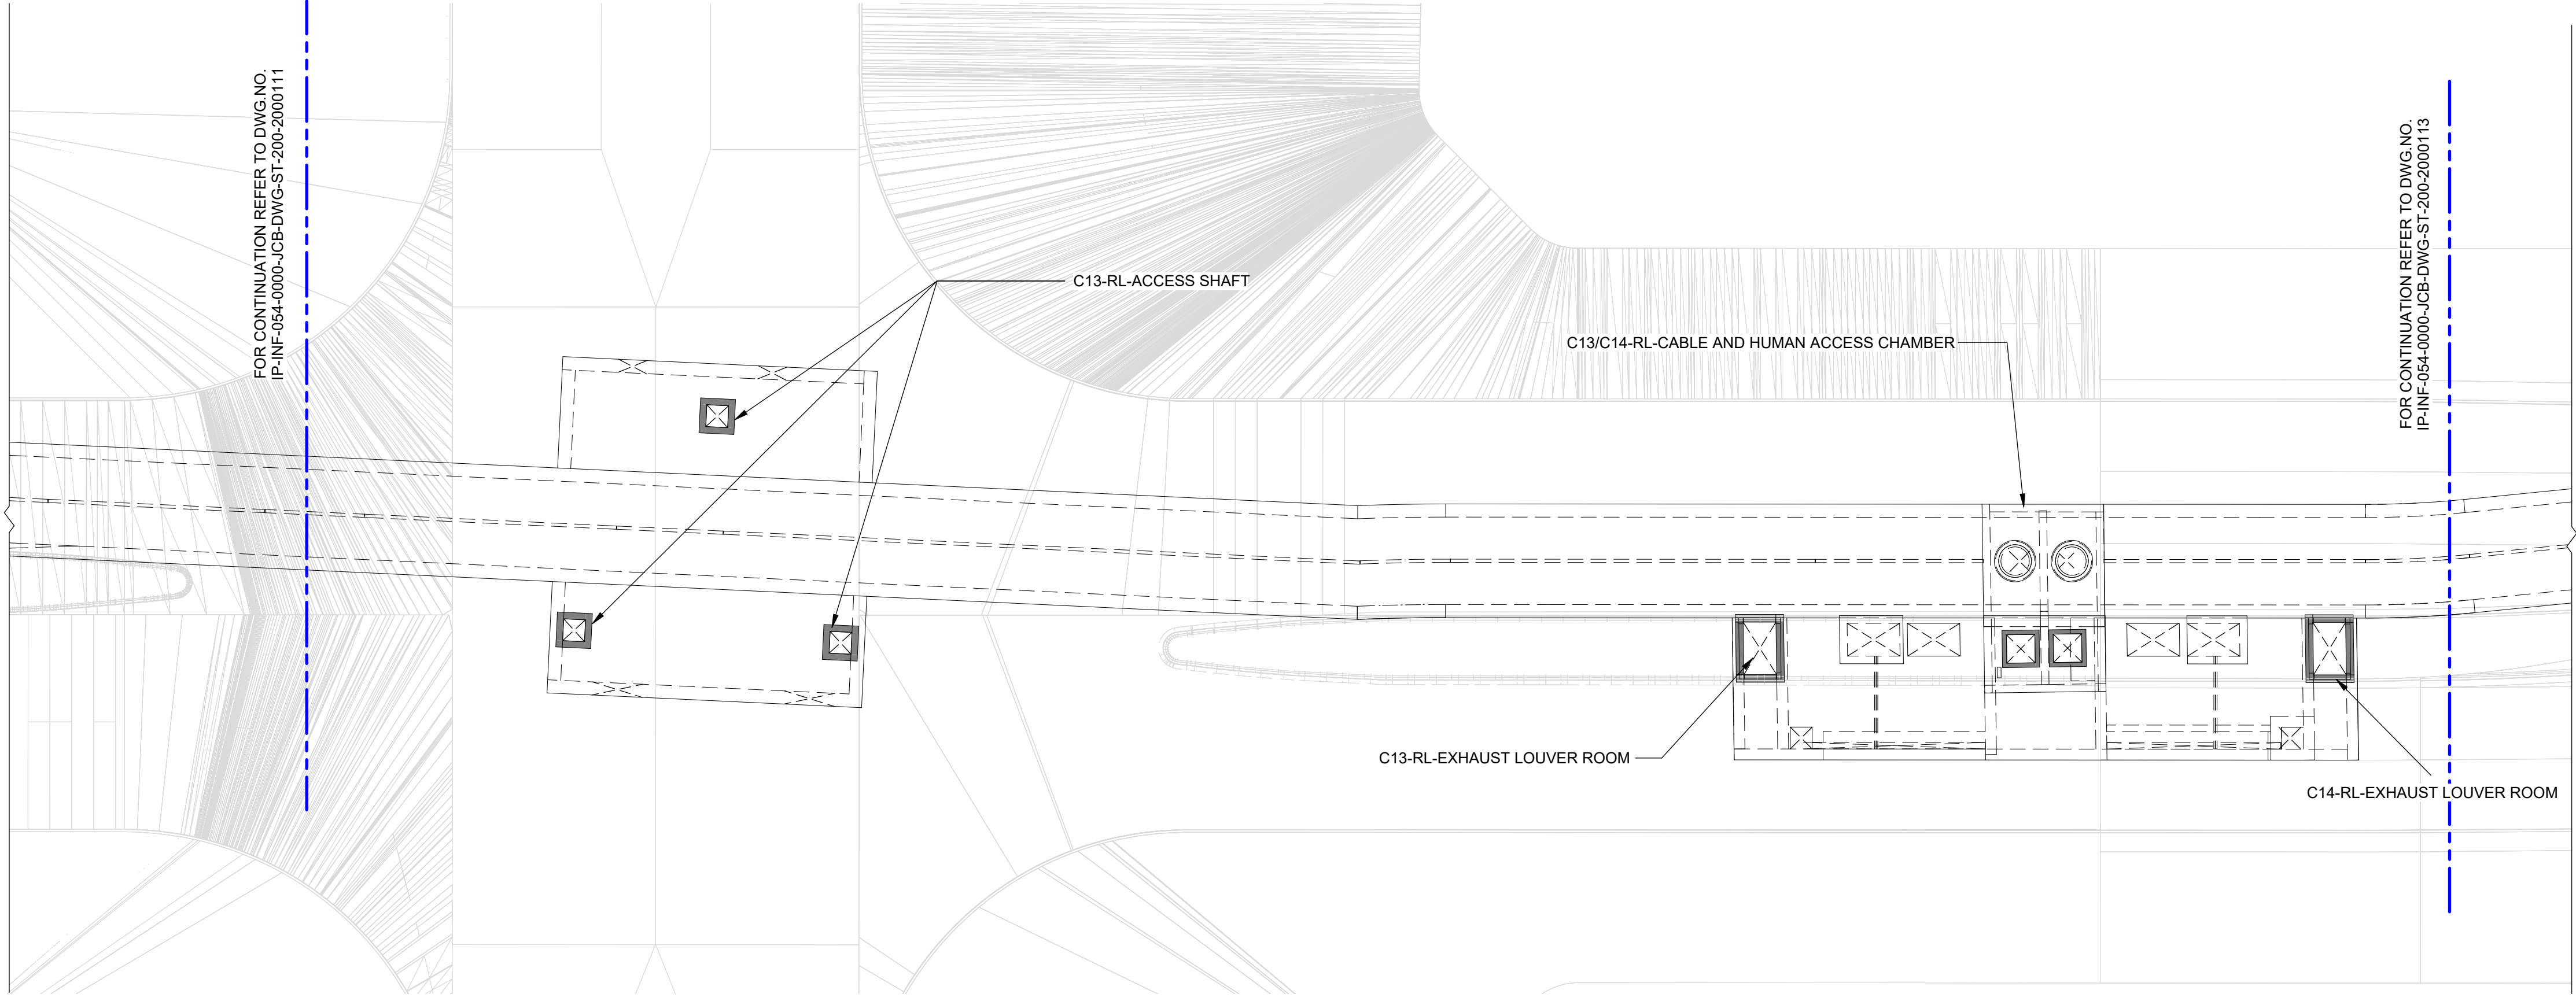

1 C-13/C-14 MV CULVERT ROAD LEVEL PLAN

1 : 200

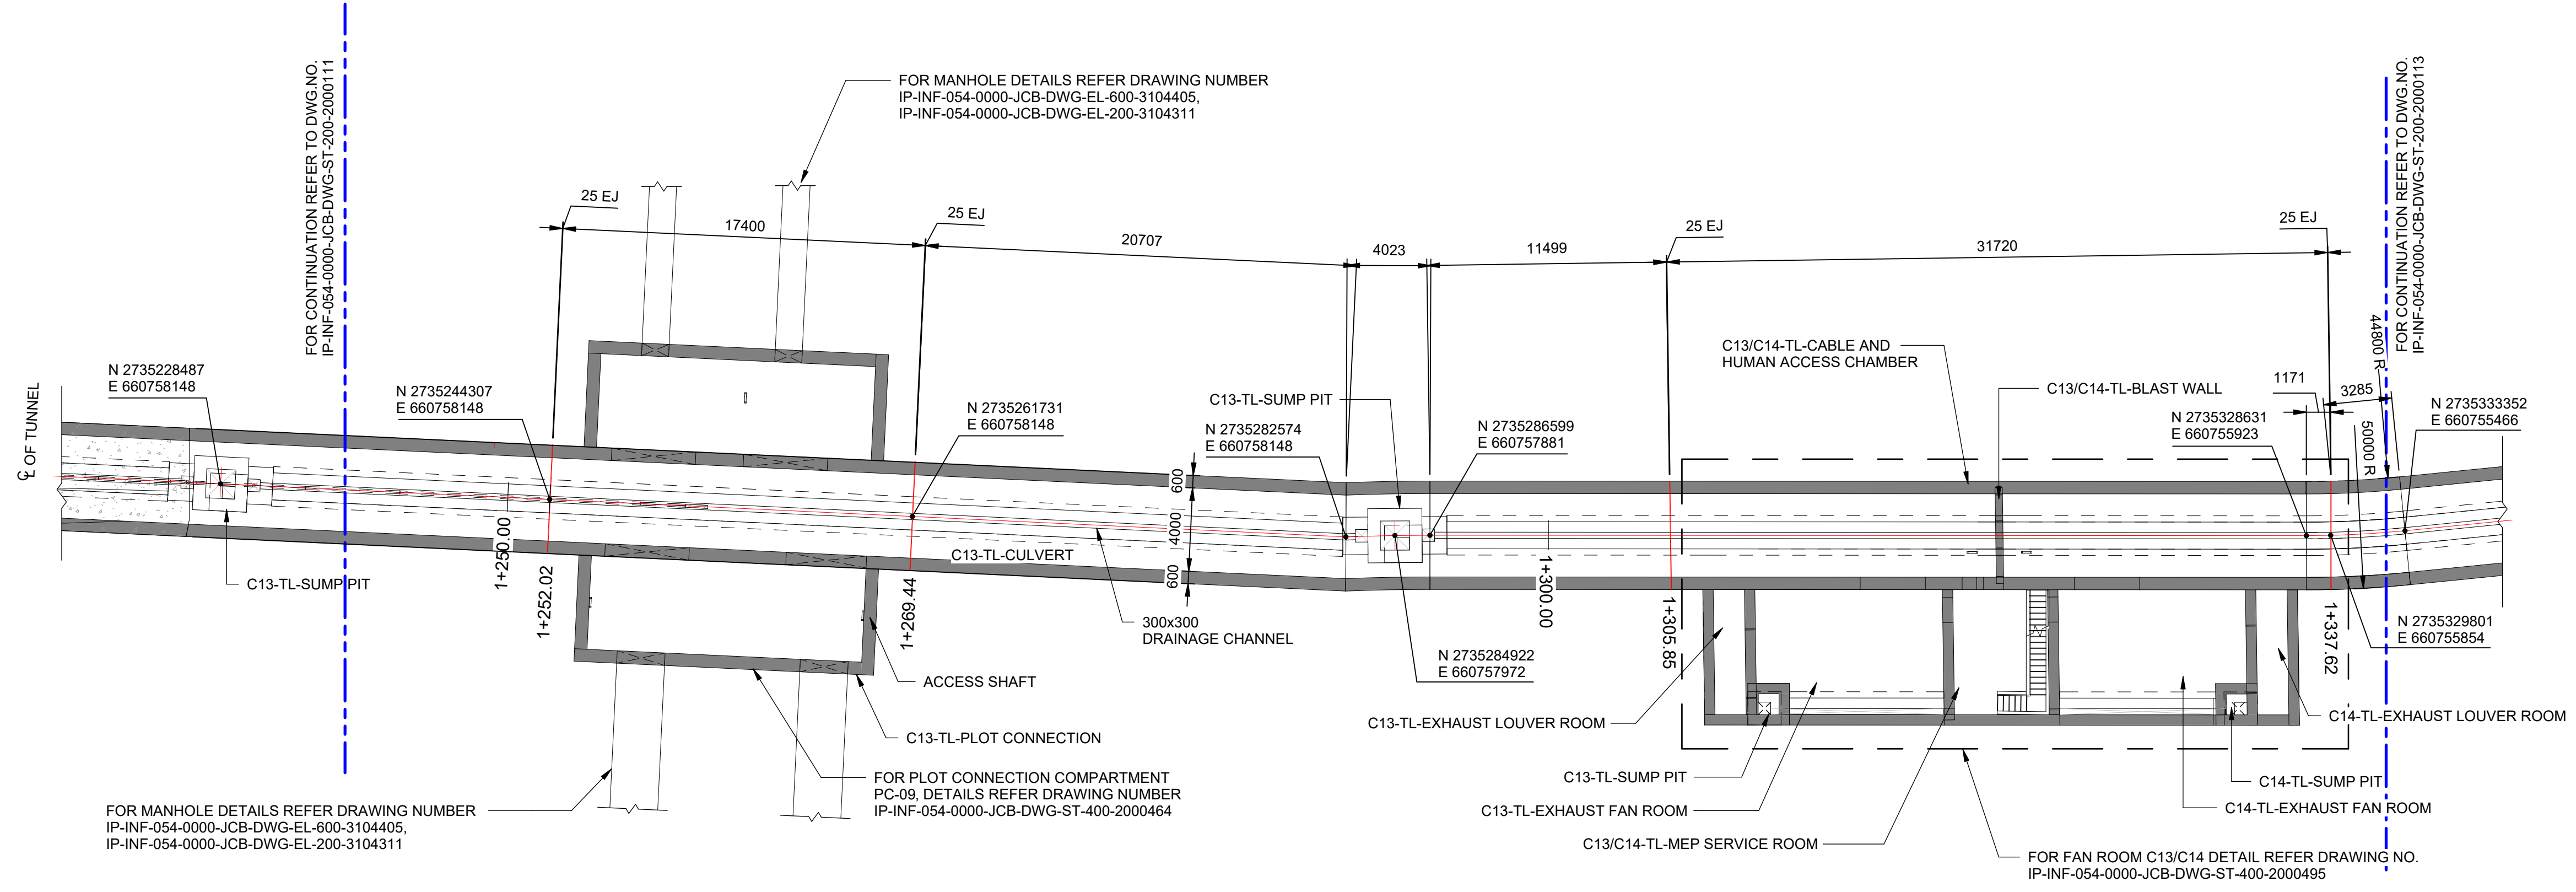

2 C-13/C-14 MV CULVERT LEVEL PLAN

1 : 200