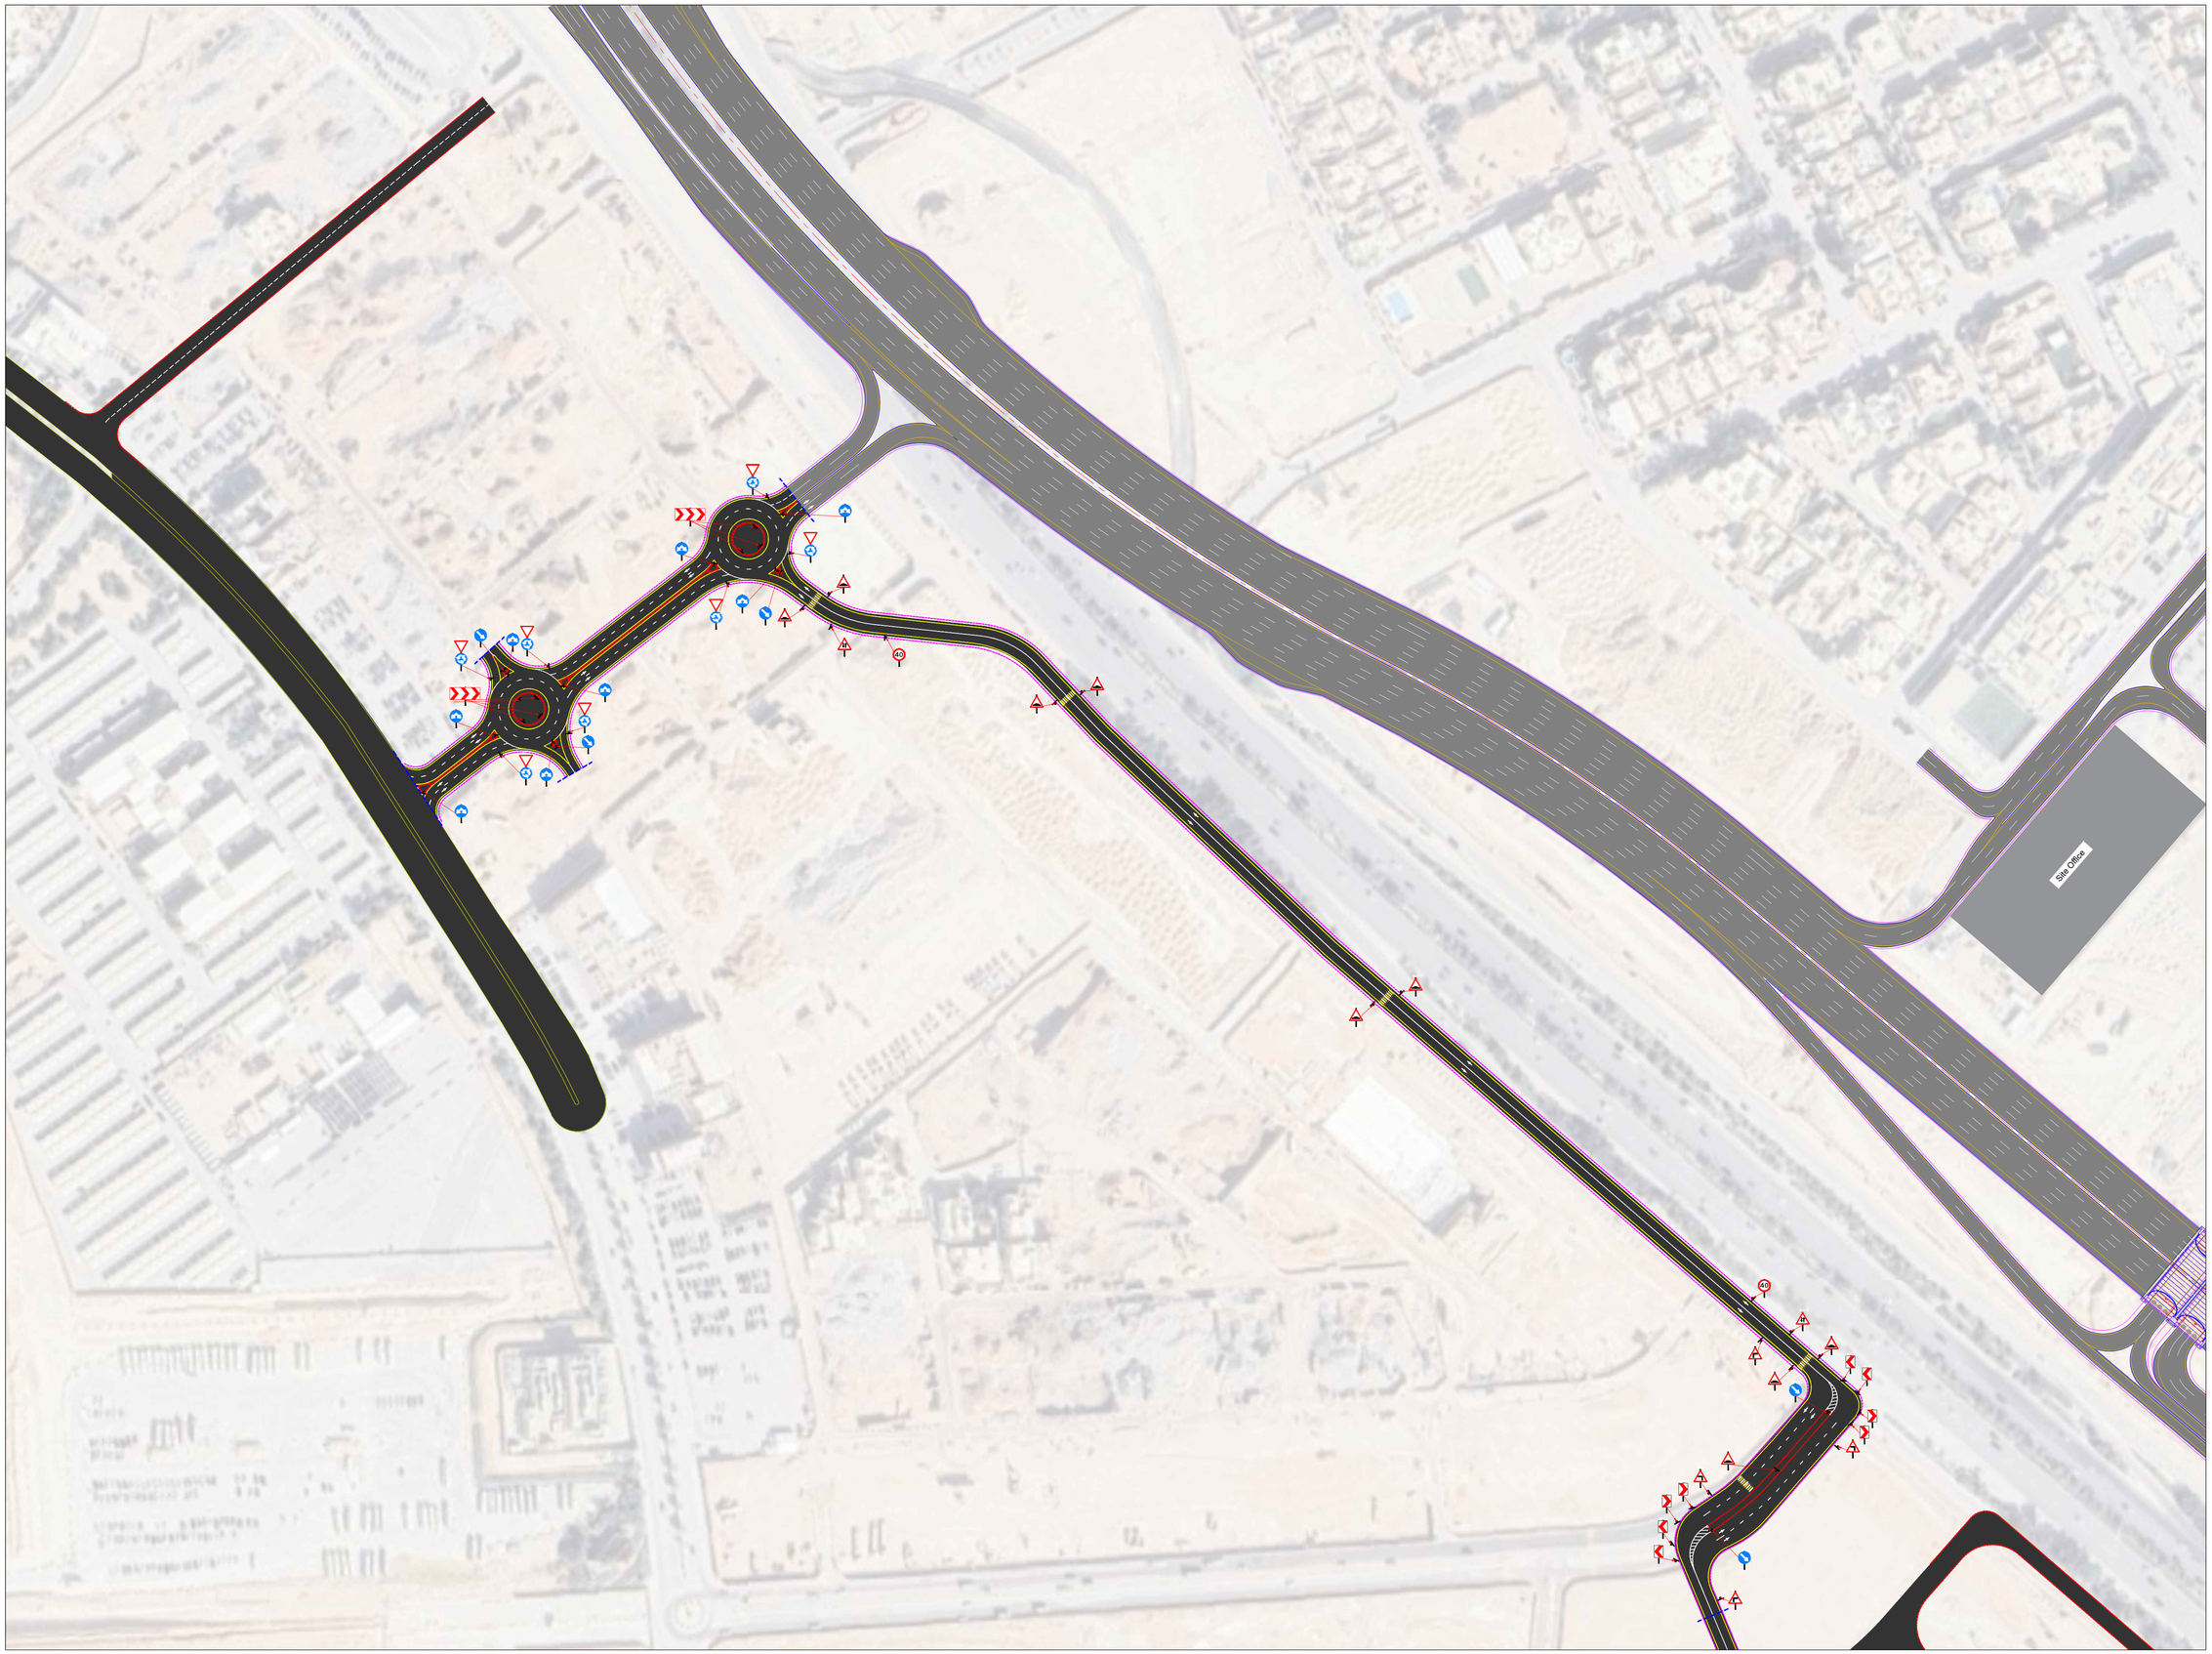


Key Plan

GENERAL NOTES:

1. THIS DRAWING IS COPYRIGHT OF DGDA AND MUST NOT BE RETAINED, COPIED OR USED WITHOUT THE BELOW CONSULTANT'S AUTHORITY.
2. DO NOT SCALE FROM THE DRAWINGS.
3. ALL DIMENSIONS ARE IN METER AND LEVELS IN METERS, UNLESS NOTED OTHERWISE ALL DIMENSIONS TO BE VERIFIED ON SITE AND APPROVED BY THE ENGINEER

Purpose of Issue	Rev.	Date	Authorised

Disclaimer: By the Consultant's review status indicated herein, the Contractor shall not be relieved of responsibility for any deviation from the requirements of the Contract documents, unless the Contractor has specifically informed the Consultant of such deviation in writing at the tie of the submission. The Contractor shall not be relieved from responsibility for errors, omissions or uncoordinated Documents and Applicable Laws. The recipient is responsible to ensure the contents of this disclaimer are understood by personnel in their organization

Notes:

1– PLANS PROVIDED ARE CONCEPTUAL AND CONTRACTOR MUST REVIEW, DETAIL FURTHER AS NECCESSARY, AND MODIFY AS PER THE EXISTING CONDITIONS.

2– CONCEPTUAL LAYOUT BASED ON THE GOOGLE SETELLITE IMAGE.

LEVEL OF DETAILS (CHECKLIST)	
BASE PLAN	
– TOPO SURVEY	
– SATELLITE IMAGE	●
– DRAWING	●
ROAD PLAN	
– ROAD CARRIAGEWAY	●
– JERSEY BARRIERS	●
– MARKING	●
SIGNAGE PLAN	
– SAFETY SIGNAGE	●
– WAYFINDING SIGNAGE	
GRADING PLAN	
– CUT AND FILL DAYLIGHT	
– SETTING OUT (X–Y)	
– SPOT ELEVATIONS (Z)	
– TABLES	
DETAILS	
– TYPICAL DETAILS	
– DIMENSIONS	
– STANDARD DRAWING	
OTHERS	
– ISOMETRIC	
– SKETCH	
– SWEPT PATH	

LEGEND:

- JERSEY BARRIERS
- ASPHALT AREA
- CARRIAGEWAY EDGE LINE MARKING
- HOARDING LINE
- EXTENT OF WORKS
- LANE MARKING (WHITE)
- NO PASSING LINE MARKING (WHITE)

Client:
DIRIYAH GATE COMPANY LIMITED

Project Management Consultant:

Supervision Consultant:

Contractor:

Traffic Consultant:
transpogroup & partner ENGINEERING CONSULTANTS
شركة ترانسبو جروب وشركاه للاستشارات الهندسية

Project:
DIRIYAH GATE DEVELOPMENT
SIDE WIDE LOGISTICS
RIYADH , KINGDOM OF SAUDI ARABIA

Drawing title:
D2
GREEN VILLAGE ROAD DIVERSION
SAFETY SIGNAGE

Original Scale:	Drawn	Checked	Authorised	Size
NTS	SG	WS	TS	A1
	Date: 01/07/2025	Date: 01/07/2025	Date: 01/07/2025	Sheet 01

Drawing Number: TG–DG2–214–002 Rev 00