
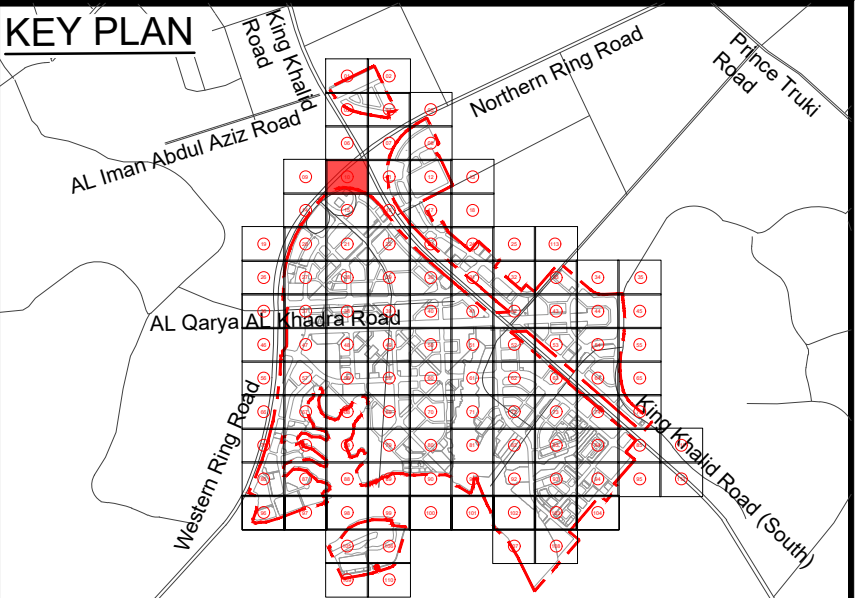


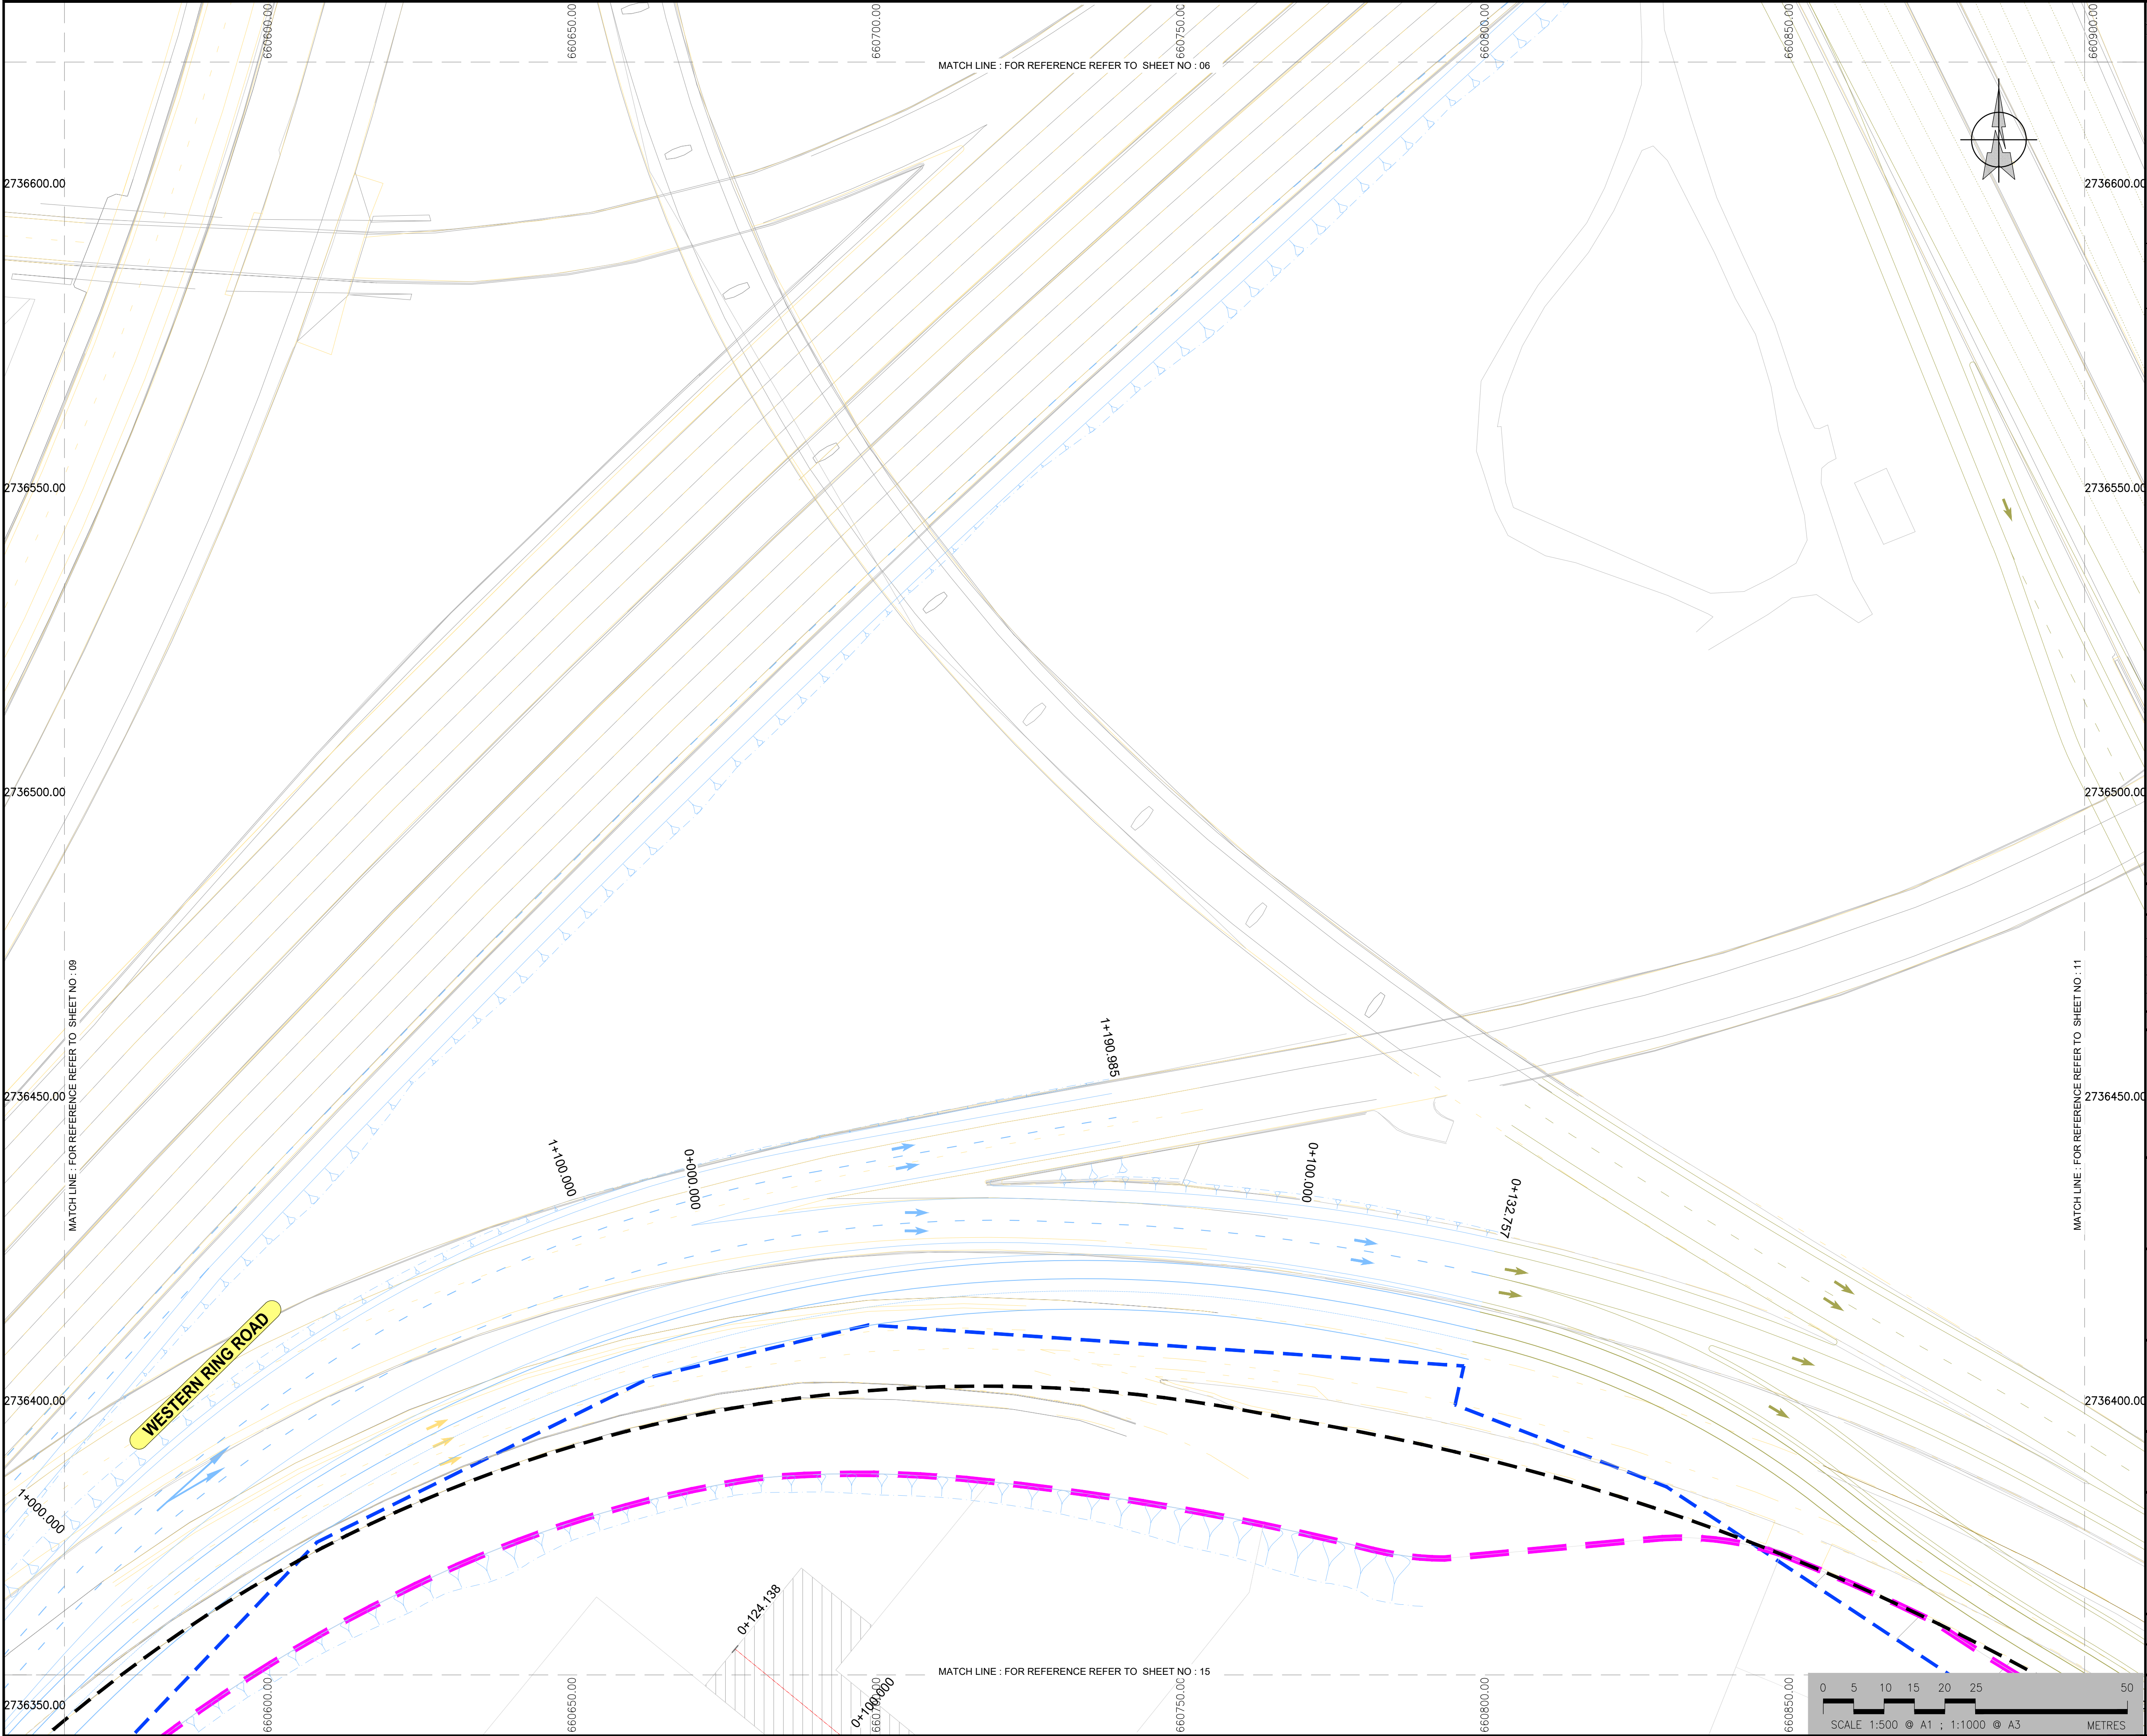

ORIENTATION

DATUM

GEODETIC DATUM: WGS-84
PROJECT SYSTEM: UTM
ZONE: 38N

- NOTES**
- ALL DIMENSIONS ARE IN METERS, UNLESS STATED OTHERWISE.
 - FOR INFRASTRUCTURE ROAD PROFILE, REFER TO DWG. SERIES: IP-INF-053-0000-JCB-DWG-TM-300-1000001.
 - FOR INFRASTRUCTURE CROSS SECTIONS, REFER TO DWG. SERIES: IP-INF-053-0000-JCB-DWG-TM-400-1000001.
 - FOR WRR ROAD LAYOUT, REF. TO DWG. SERIES: IP-INF-053-0000-JCB-DWG-TM-200-0015001.
 - FOR KKR ROAD LAYOUT, REF. TO DWG. SERIES: IP-INF-053-0000-JCB-DWG-TM-200-0014001.

LEGEND

- ROW
- PROJECT BOUNDARY
- LOW
- LIMIT OF WORKS
- PACKAGE I BOUNDARY
- ROAD CENTER LINE
- PROPOSED UPSTAND KERB
- ROAD MARKING
- WRR ROAD LAYOUT
- KKR ROAD LAYOUT
- DESIGN BY OTHERS
- BUS STOP
- ROAD ASPHALT
- PLOT ACCESS
- PARKING AREA
- MEDIAN AND ISLANDS
- EDGE ZONE
- PEDESTRIAN
- VERGE/ PLANTING
- CYCLE PATHWAY
- RAISED TABLE
- RAISED JUNCTION
- PEDESTRIAN BRIDGES / UNDERPASS
- COMMON SPACE
- FOOTPATH
- PACKAGE II AREA

Project Stage

PRELIMINARY DESIGN

THE USE OF THIS DOCUMENT FOR CONSTRUCTION PURPOSES IS SUBJECT TO AND CONDITIONAL UPON RECEIPT OF THE APPROPRIATE STATUTORY AUTHORITY APPROVAL

FOR TENDER	A	04/05/23	AJ
Description	Rev	Date	Authorises

Project:

**DIRIYAH GATE PHASE II
& KING KHALID ROAD
INFRASTRUCTURE DESIGN
KINGDOM OF SAUDI ARABIA**

Client:

DIRIYAH GATE COMPANY LIMITED
8500 Prince Sattam Ibn Abdulaziz
Al Shohda Dist. AD DIRIYAH 12572 - 4000
Kingdom Of Saudi arabia

Lead Consultant:

Jacobs
P.O. Box 360, Dubai U.A.E.
www.jacobs.com

Jacobs

Subconsultant:

Package:

**DIRIYAH GATE PHASE II
INFRASTRUCTURE – PACKAGE 1**

Drawing title:

**INFRASTRUCTURE
ROAD LAYOUT
SHEET 10 OF 113**


Drawn	MG	Checked	MM	Verified	AVH	Approved	AJ/EB	Size	A1
Date:	04/05/2023	Date:	04/05/2023	Date:	04/05/2023	Date:	04/05/2023	Scale	1:500

Drawing Number:

IP-INF-053-0000-JCB-DWG-TM-200-01100010

Rev

A

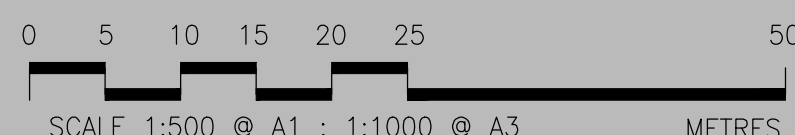

IP-INF-053-0000-JCB-DWG-TM-200-01100010.dwg